二楼功能分区与家具布置图

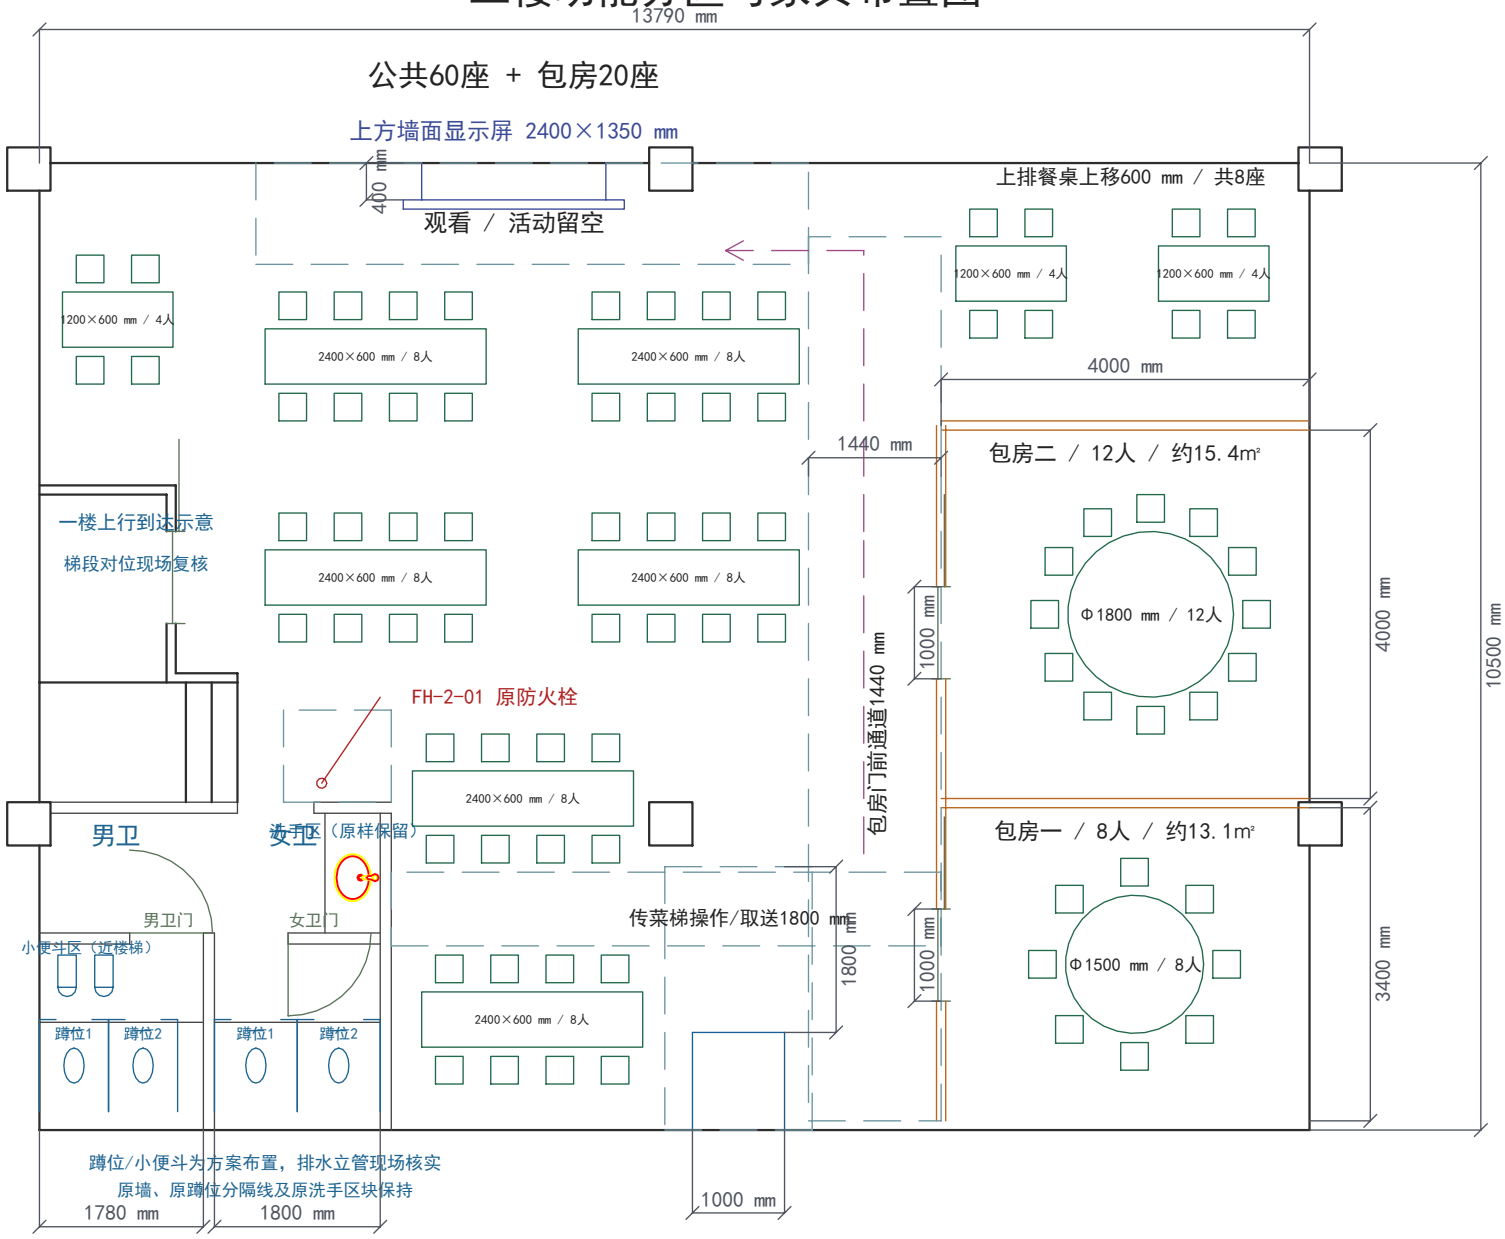

本图所有尺寸单位：mm；模型1:1，PDF适合页面打印

美莱食堂 V1.5 | 600mm桌深 / 300mm凳面 | 黑底高对比DWG

实线：结构及桌凳；长虚线：净空；楼梯踏步和洁具图符为标识示意

最小桌组人体包络净距800 mm；门前、消防与传菜梯操作面不摆桌