二楼尺寸标注平面图

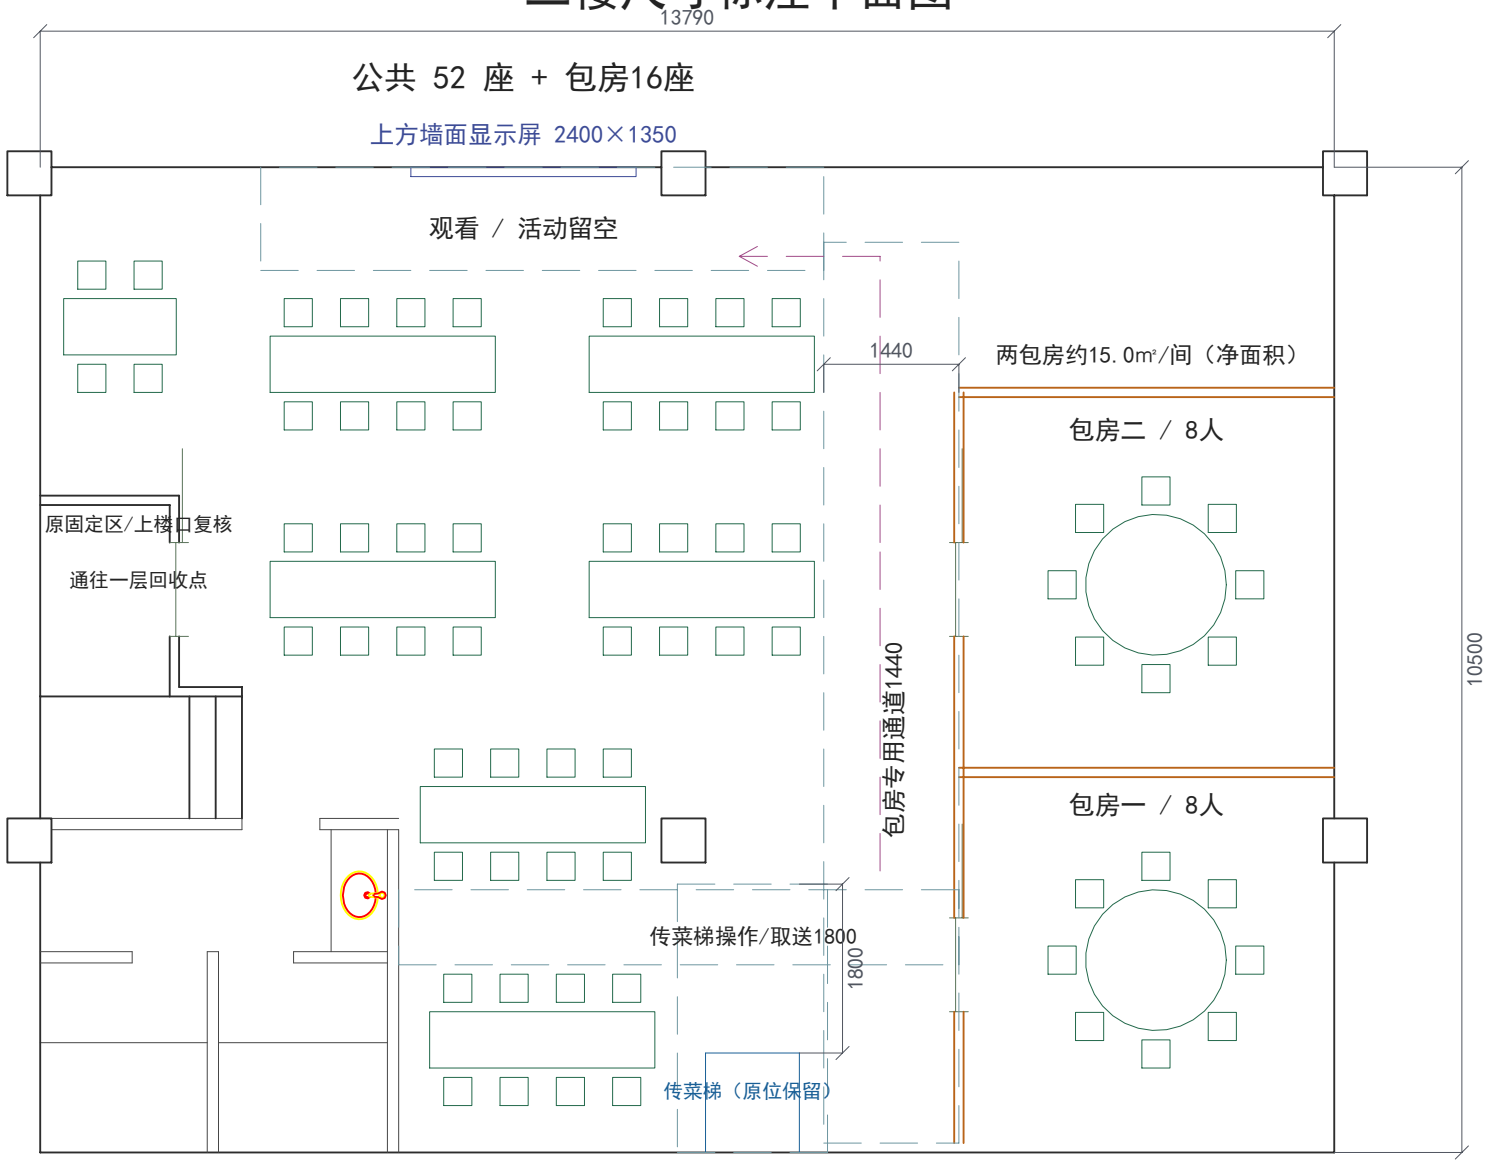

原男/女卫生间及蹲位原样保留

美莱食堂 | V1.2 简洁优化 | 单位mm | 模型1:1；PDF适合页面打印

深绿：桌凳　蓝：原传菜梯/设备　橙：新墙/两人打菜　虚线：必须留空

桌边留100+凳面300+人体余量100；外侧次通道≥800，主通道优先1800

拆墙按业主可拆隔墙意向表达；原图未提供结构证明，施工前核实