
一层平面图

尺寸单位：mm　比例：1:100

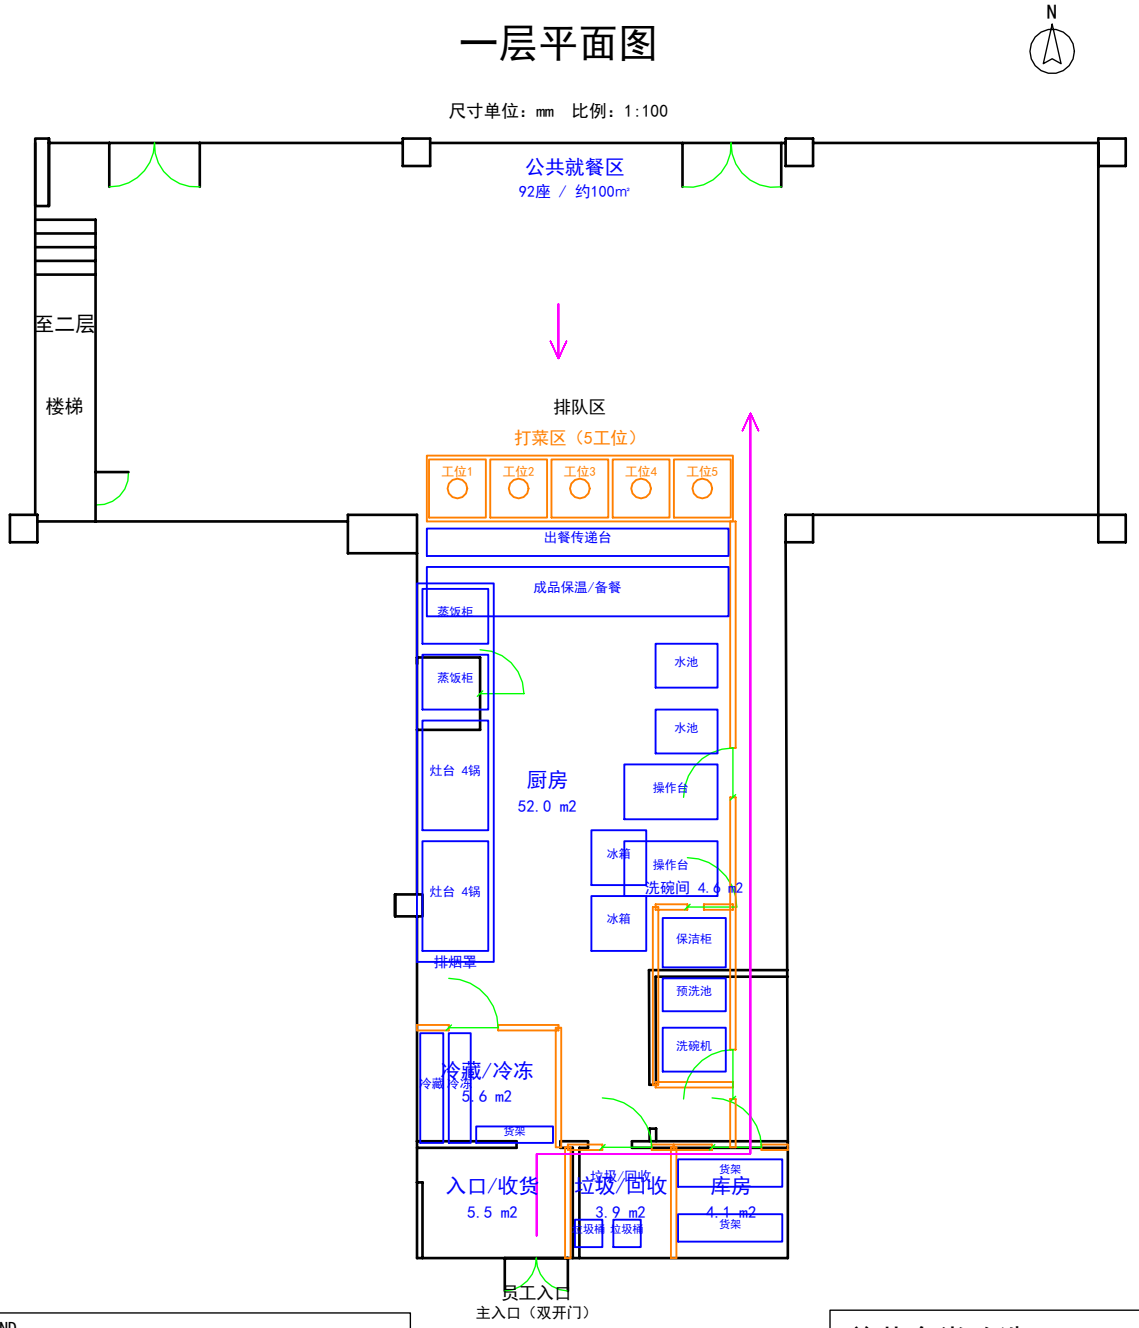

图例 / LEGEND

- 原有墙体/结构
- 新增隔墙（100mm）
- 拆除墙体（待结构复核）
- 家具/餐桌椅
- 厨房/服务设备
- 人员/物流路径

注：1. 尺寸单位mm，比例1:100。
2. 红色为拆除，橙色为新建。
3. 原始DWG保留；拆改、消防、结构、机电需专业复核。
4. 厨房/包房/显示屏设备尺寸为方案参考，施工前复核。

美莱食堂改造

一层平面图

图号：1F_A_kitchen
比例：1:100
单位：mm　版本：V1.1　日期：2026-10-18